
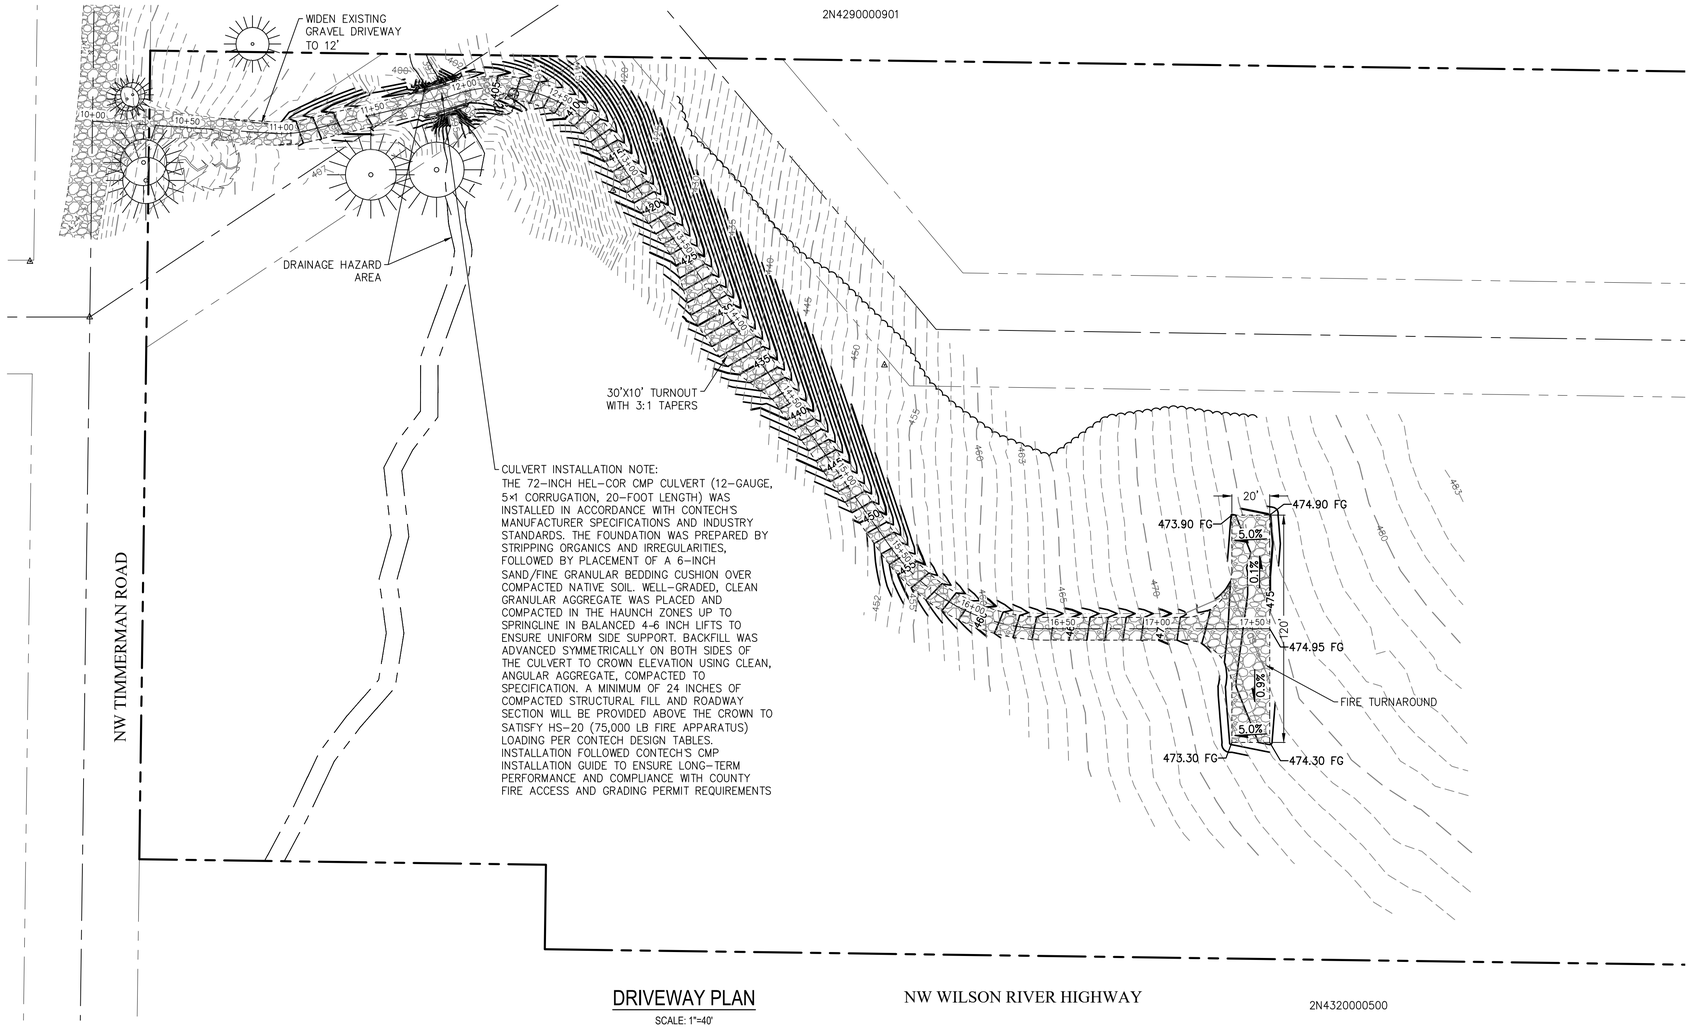



DRIVEWAY PLAN

SCALE: 1"=40'

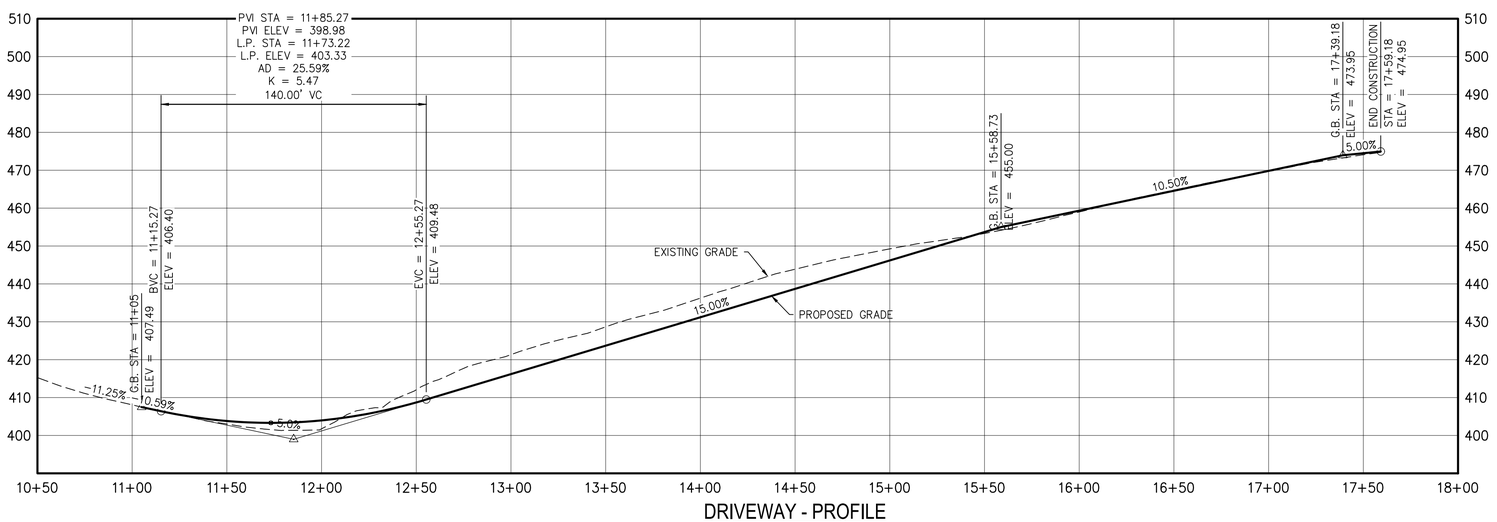

DRIVEWAY - PROFILE

SCALE: 1"=40' H, 1"=20' V

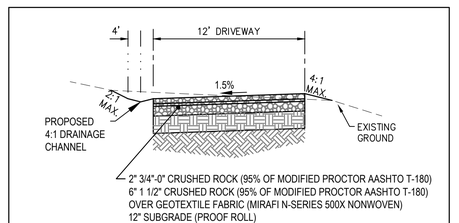

GRAVEL DRIVEWAY SECTION

N

40' 0 20' 40' 80'

SCALE: 1" = 40'

LEGEND

- BOUNDARY LINE
- EASEMENT
- 104 EXISTING 1' CONTOUR LINE
- 105 EXISTING 5' CONTOUR LINE
- EXISTING CENTER LINE OF RIGH-OF-WAY
- EXISTING TREE
- 104 PROPOSED 1' CONTOUR LINE
- 105 PROPOSED 5' CONTOUR LINE

REVIEWED FOR CODE COMPLIANCE
VALIDITY OF PERMIT
The issuance or granting of a permit or approval of plans, specifications and computations shall not be construed to be a permit for, or an approval of, any violation of the provisions of this code or of any other ordinance of the jurisdiction
DATE 1/7/2026
BLDG-2514996

NW TIMM
TAX MAP
TAX
FOREST GI

DRIVEWAY PLAN AND PROFILE

REVISIONS

NO.	DATE	DESCRIPTION

EMERIO
ENGINEERING • SURVEYING • DESIGN
6445 SW FALLBROOK PLACE, SUITE 100
BEAVERTON, OREGON 97008
TEL: (503) 746-8812
FAX: (503) 639-9592
www.emeriodesign.com

REGISTERED PROFESSIONAL ENGINEER
95296PE
DIGITALLY SIGNED
2025.10.23 13:47:30 -07'00'
OREGON NOVEMBER 10, 2015
ALFREDO PEREZ-LOZANO
EXPIRES: 12/31/2026

SHEET 3 OF 4

FILE:P:\1916-001 Timmerman Road\dwg\civil\1916-001_03dwg, Layout: 3 DRIVEWAY PLAN AND PROFILE, Plot Date: 10/22/2025 10:28 AM, by: Kyung Han