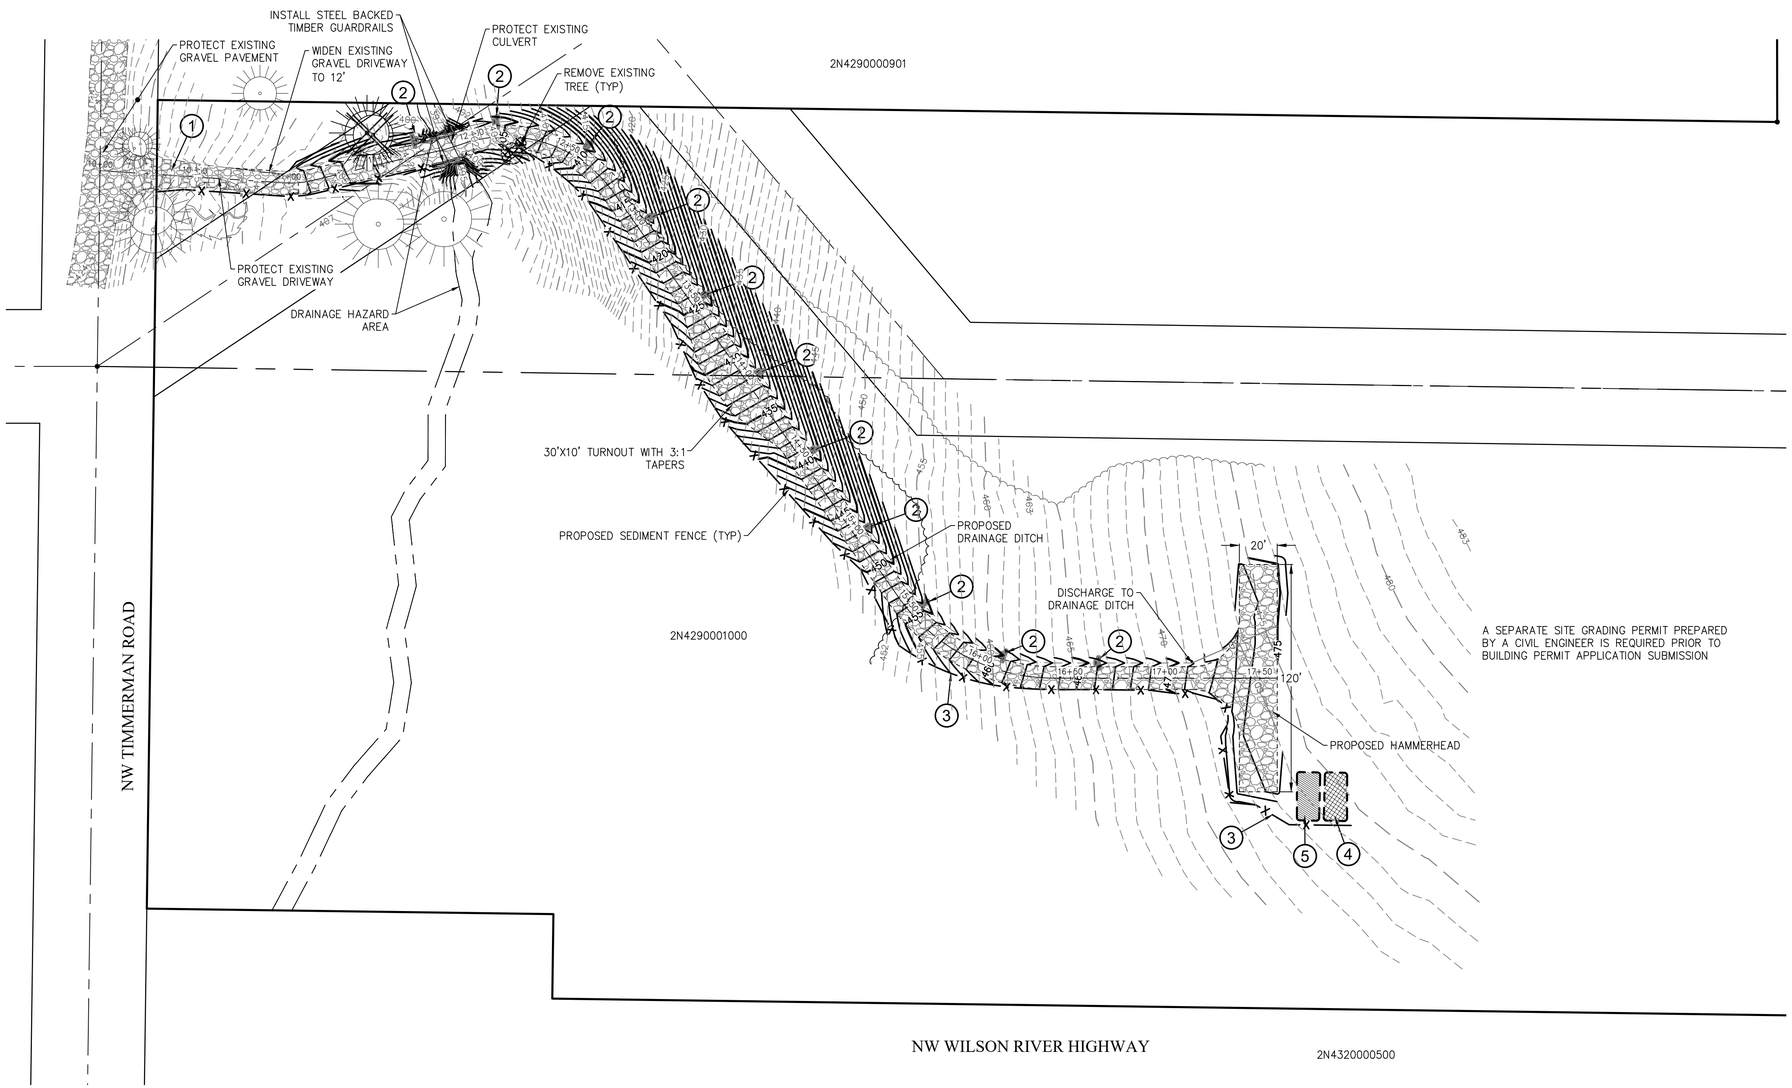


GRADING & EROSION CONTROL PLAN

SCALE: 1"=40'

N

40' 0 20' 40' 8

SCALE: 1" = 40'

REVIEWED FOR CODE COMPLIANCE
VALIDITY OF PERMIT
The issuance or granting of a permit or approval of plans, specifications and computations shall not be construed to be a permit for, or an approval of, any violation of the provisions of this code or of any other ordinance of the jurisdiction
DATE 1/7/2026
BLDG-2514996

LEGEND

- BOUNDARY LINE
- EASEMENT
- 104 EXISTING 1' CONTOUR LINE
- 105 EXISTING 5' CONTOUR LINE
- EXISTING CENTER LINE OF RIGH-OF-WAY
- SD SD PROPOSED STORM LINE
- SS SS PROPOSED SANITARY LINE
- W W PROPOSED WATERLINE
- EXISTING TREE
- 104 PROPOSED 1' CONTOUR LINE
- 105 PROPOSED 5' CONTOUR LINE
- X X PROPOSED SEDIMENT FENCE

EROSION CONTROL NOTES

1. USE EXISTING DRIVEWAY AS CONSTRUCT CONSTRUCTION ENTRANCE
2. INSTALL CHECK DAM
3. INSTALL SEDIMENT FENCE
4. STOCK PILE AREA
5. STAGING AREA

NW TIMMERMAN ROAD
TAX MAP
TAX
FOREST GI

GRADING & EROSION CONTROL PLAN

REVISIONS

NO.	DATE	DESCRIPTION

EMERIO
ENGINEERING • SURVEYING • DESIGN
6445 SW FALLBROOK PLACE, SUITE 100
BEAVERTON, OREGON 97008
TEL: (503) 746-8812
FAX: (503) 639-9160
www.emeriodesign.com

REGISTERED PROFESSIONAL ENGINEER
95296PE
OREGON
NOVEMBER 10, 2015
ALFREDO PEREZ-LLANOS
EXPIRES: 12/31/2026
DIGITALLY SIGNED 2025.10.23 13:47:14-07'00'

SHEET 2 OF 4

FILE:P:\1916-001 Timmerman Road\dwg\civil\1916-001_02grad, Layout: 2 GRADING & EROSION CONTROL PLAN, Plot Date: 10/22/2025 10:28 AM, by: Kyung Hon